
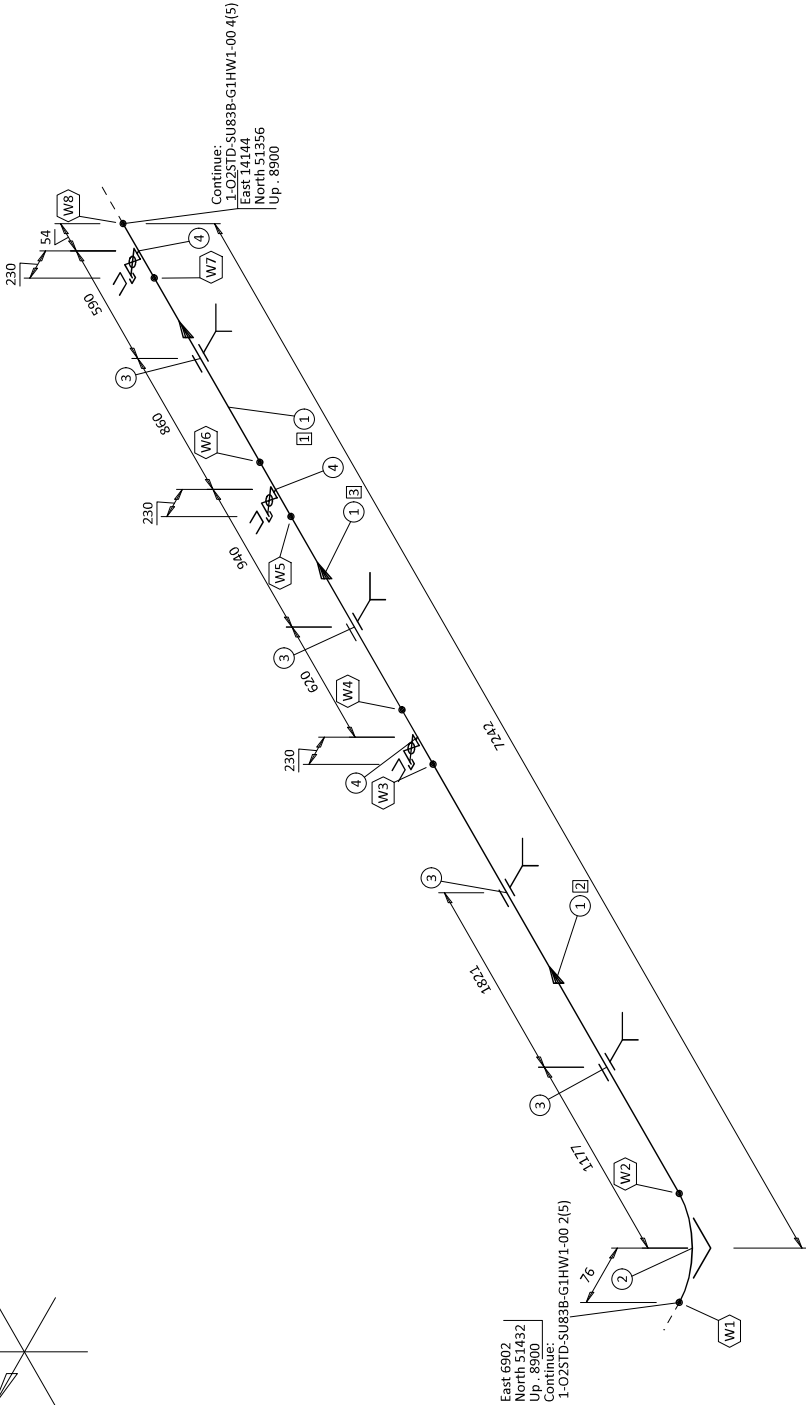


Bill of Materials

Part	Description	Material Code	Size	Material	Pcs./Length	Unit	Mass Weight
1	TUBE		1" x 1.65	EN1.4404 SMLS	6.85	0.00	6.72
2	90° ELBOW		1"	EN1.4404	1		0.00
3	cush-a-clamp 1"	01ET020	1"		4		0.00
4	VALVE BA-S1.13	8855640510P1001	1" x 1/2"		3		0.00

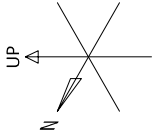

East 6902
North 51432
Up . 8900
Continue:
1-O2STD-SU83B-G1HW1-00 2(S)

Continue:
1-O2STD-SU83B-G1HW1-00 4(S)
East 14144
North 51356
Up . 8900

DISEGNI DI RIFERIMENTO:
PIANTE: 0P01-R3FPG-1EFA008
SEZIONI: 0P01-R3FPG-7301013

Weld & Joint Information

Weld	Size	Weld Type
W1	1"	BW
W2	1"	BW
W3	1"	BW
W4	1"	BW
W5	1"	BW
W6	1"	BW
W7	1"	BW
W8	1"	BW

Cut List

CutN°	Part N°	Length
1	1	1342
2	1	4048
3	1	1452




PIPELINE N: 1-O2STD-SU83B-G1HW1-00 3(5)

Site Plan

Building Codes - R3 Project:

- A = Overall / Entire Project
- C = CUR
- E = Entrance
- F = Fabrication
- G = Gas
- H = Hazards
- P = Support
- S = Scrubber

PROJECT
MOUNTAIN

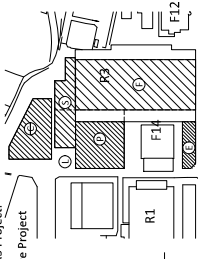

Drawing symbols

- ☐ SPOOL NAME ☐ PART NUMBER
- ☐ WELDING NUMBER ☐ CUT NUMBER



REV. N°

E-3884

DATE

2024.03.05

5

A2